


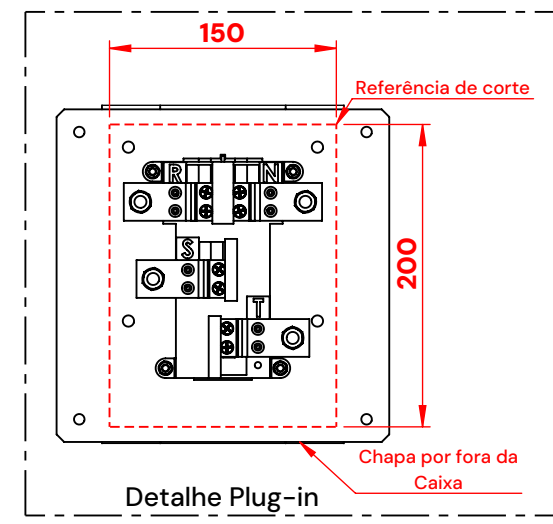
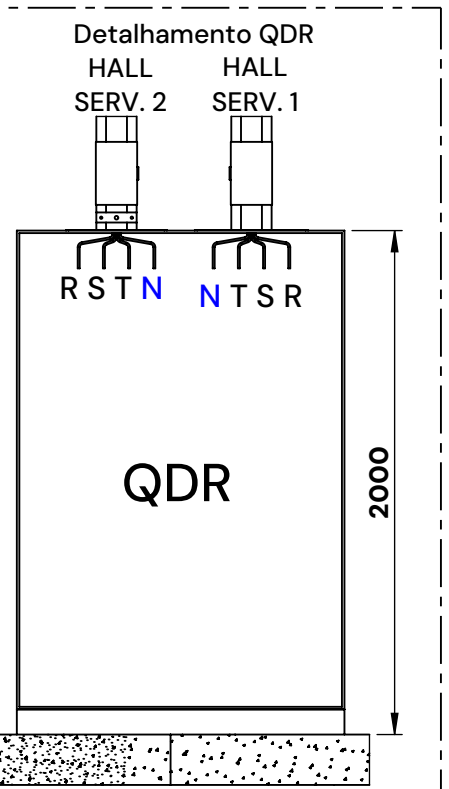
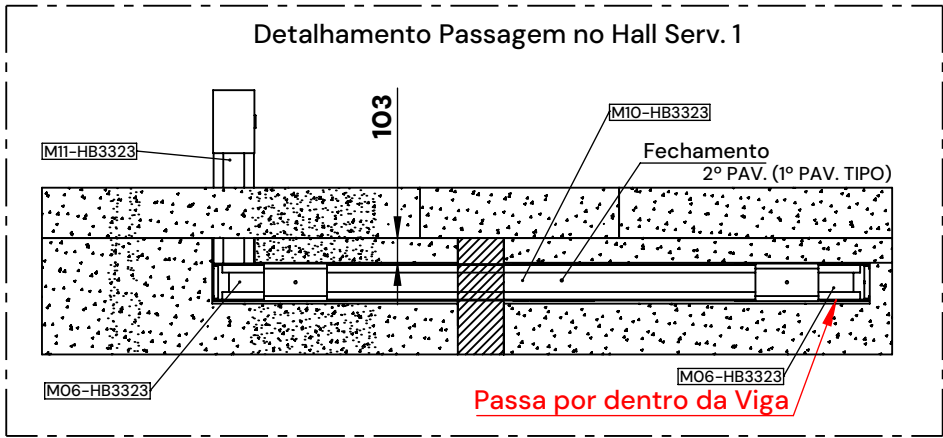
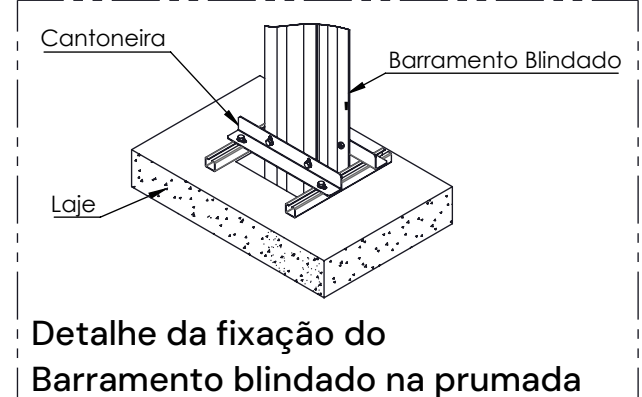
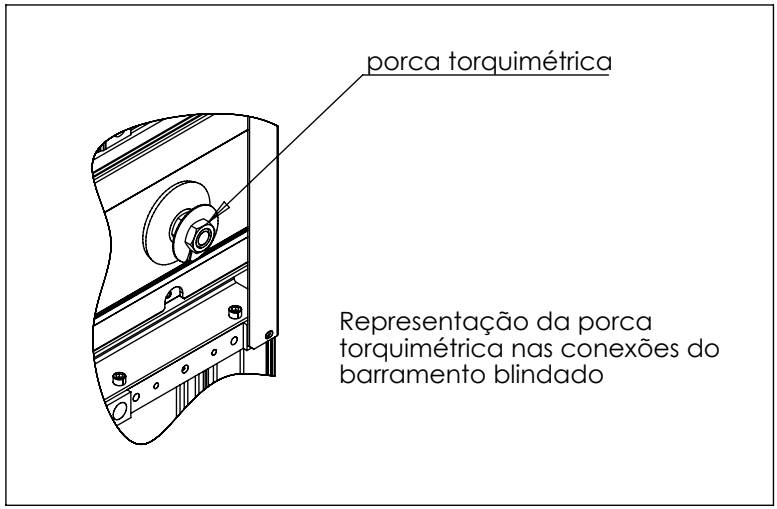
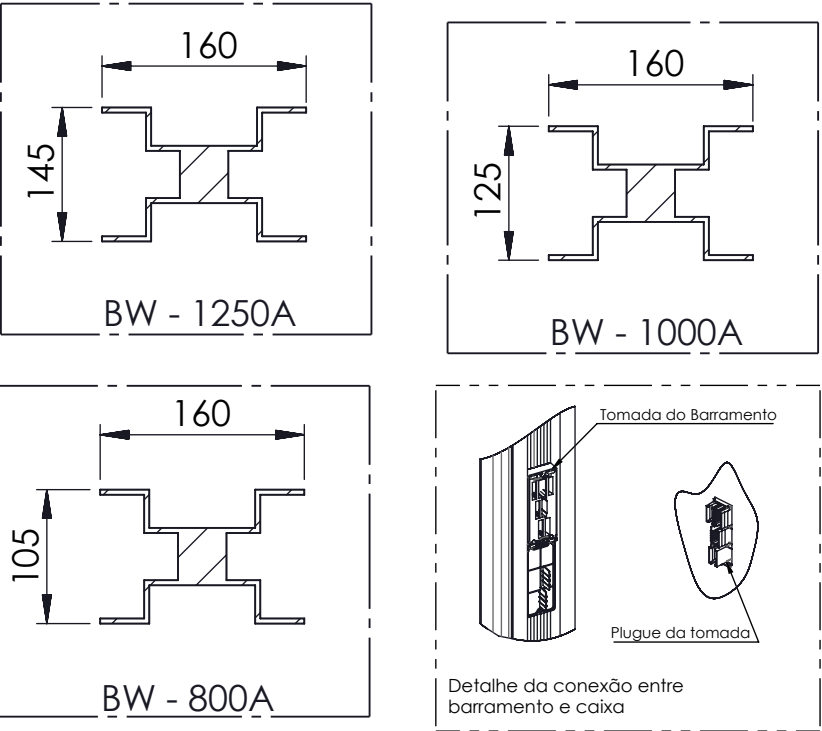
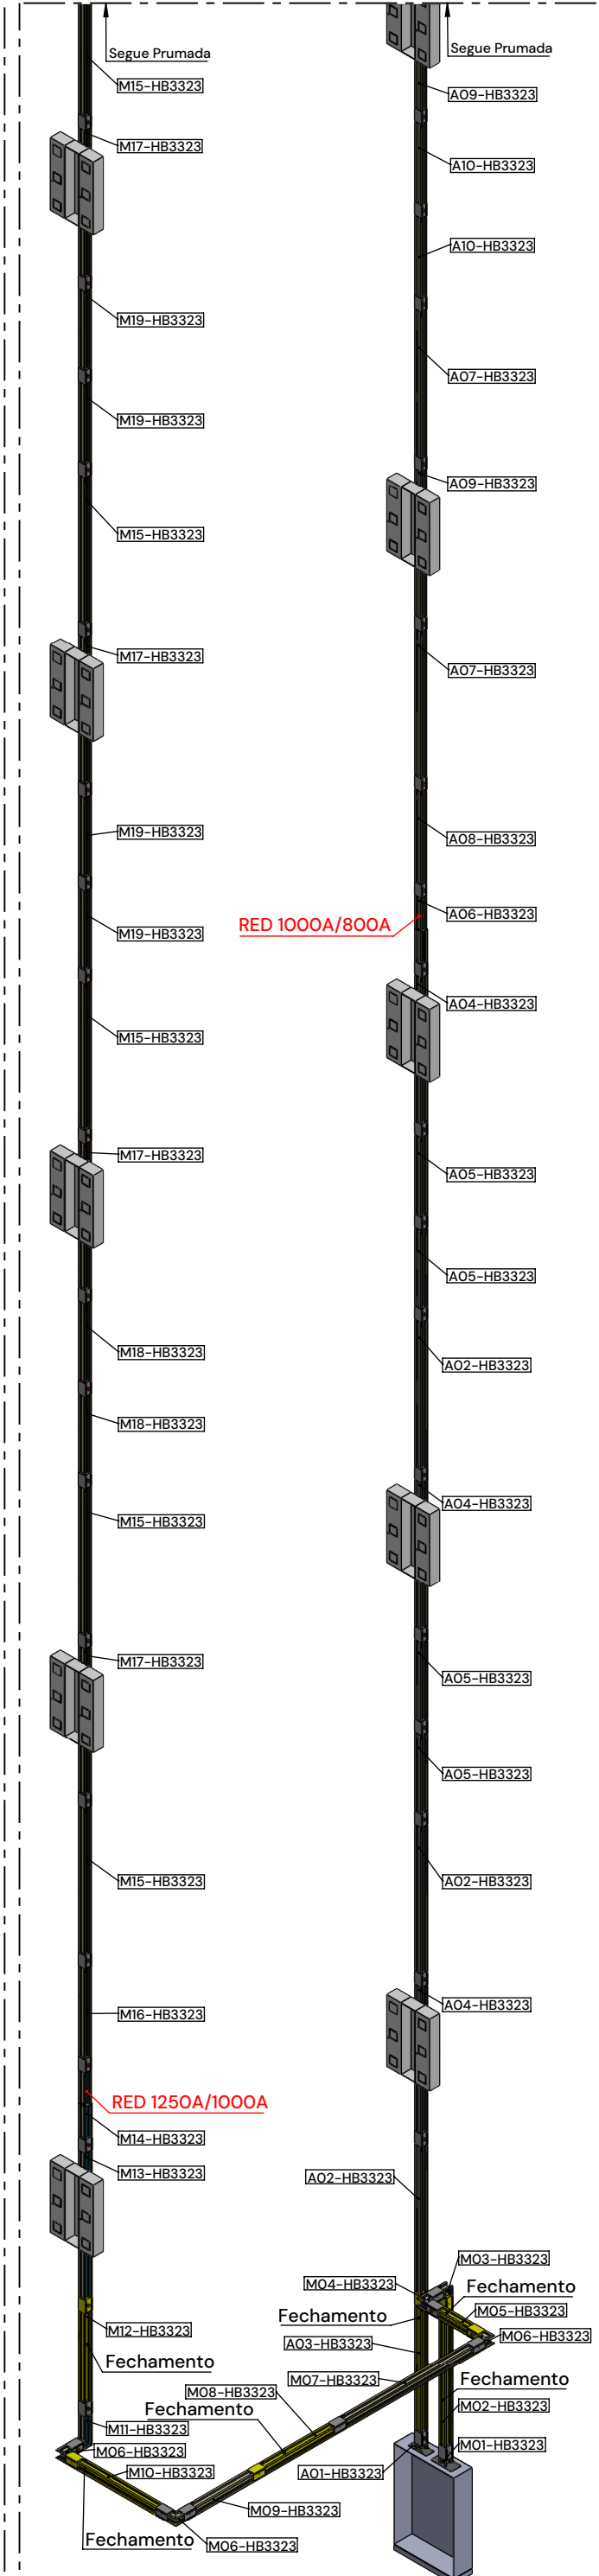


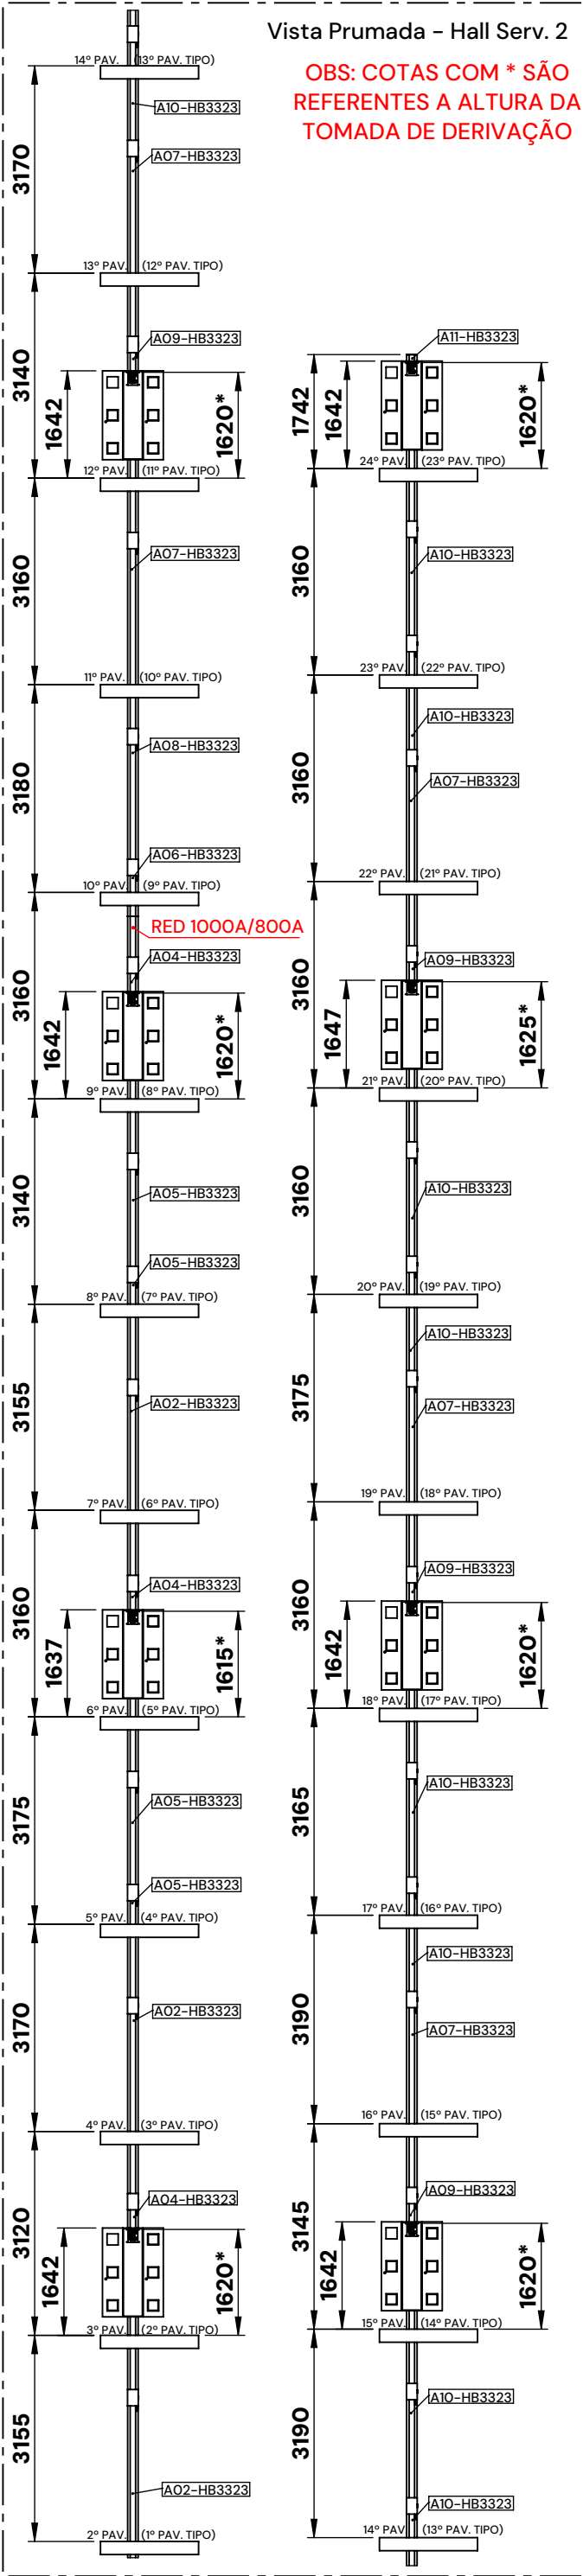

Vista Superior – Pav. 1 (Pav. Térreo)

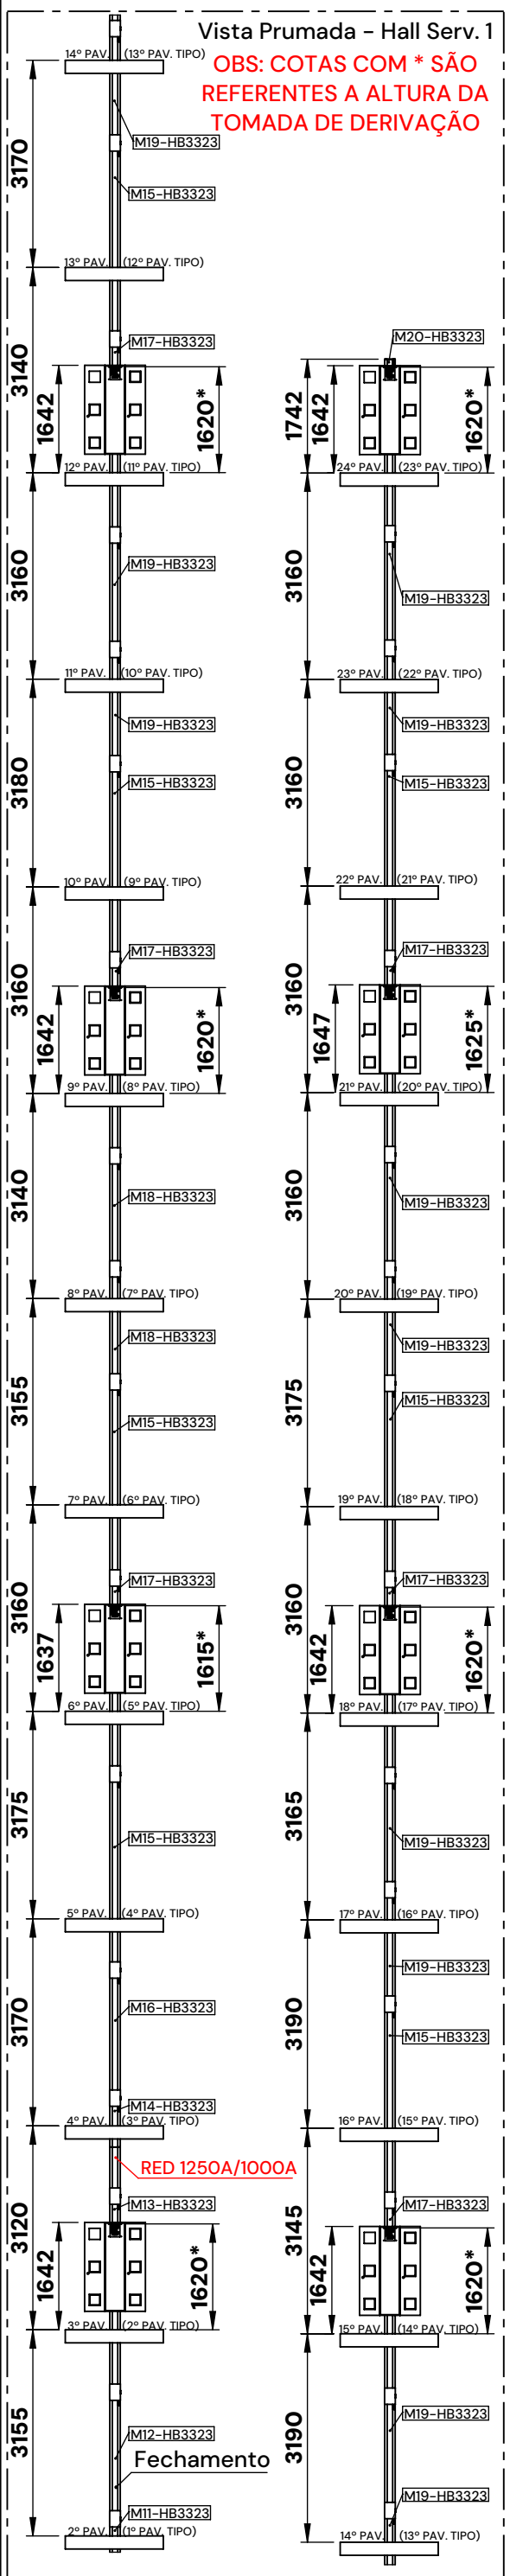

100-031	16	100-031	Suporte Montado p/ Plugue 2 pinças até 250A
M20-HB3323	1	EDF 60-2545-120	Elemento de Derivação Final 1000A - Comp. 2545 - Plugue 120
M19-HB3323	10	ER 60-1750	Elemento Reto 1000A - Comp. 1750
M18-HB3323	2	ER 60-1730	Elemento Reto 1000A - Comp. 1730
M17-HB3323	6	ED1 60-3000-300	Elemento de Derivação 1000A - Comp. 3000 - Plugue 300
M16-HB3323	1	ER 60-1960	Elemento Reto 1000A - Comp. 1960
M15-HB3323	7	ER 60-3000	Elemento Reto 1000A - Comp. 3000
M14-HB3323	1	RE 60-80-624-624	Elemento de Redução 1250A/1000A - Comp. 624 x 624
M13-HB3323	1	ED1 80-3000-300	Elemento de Derivação 1250A - Comp. 3000 - Plugue 300
M12-HB3323	1	ER 80-1938	Elemento Reto 1250A - Comp. 1938 - Fechamento
M11-HB3323	1	CT2 80-585-185	Cotovelo Tipoll - 1250A - Comp. 585 x 185
M10-HB3323	1	ER 80-1950	Elemento Reto 1250A - Comp. 1950 - Fechamento
M09-HB3323	1	ER 80-1500	Elemento Reto 1250A - Comp. 1500
M08-HB3323	1	ER 80-1750	Elemento Reto 1250A - Comp. 1750 - Fechamento
M07-HB3323	1	ER 80-3000	Elemento Reto 1250A - Comp. 3000
M06-HB3323	3	CT1 80-200-200	Cotovelo Tipol - 1250A - Comp. 200 x 200
M05-HB3323	1	ER 80-890	Elemento Reto 1250A - Comp. 890 - Fechamento
M04-HB3323	1	CT1 80-200-200	Cotovelo Tipoll - 1250A - Comp. 200 x 200
M03-HB3323	1	CT2 80-185-185	Cotovelo Tipoll - 1250A - Comp. 185 x 185
M02-HB3323	1	ER 80-2785	Elemento Reto 1250A - Comp. 2785 - Fechamento
M01-HB3323	1	FLP 80-100	Flange Padrão - 1000A - Comp. 100
A11-HB3323	1	EDF 40-2545-120	Elemento de Derivação Final 800A - Comp. 2545 - Plugue 120
A10-HB3323	8	ER 40-1750	Elemento Reto 800A - Comp. 1750
A09-HB3323	4	ED1 40-3000-300	Elemento de Derivação 800A - Comp. 3000 - Plugue 300
A08-HB3323	1	ER 40-2000	Elemento Reto 800A - Comp. 2000
A07-HB3323	5	ER 40-3000	Elemento Reto 800A - Comp. 3000
A06-HB3323	1	RE 40-60-624-624	Elemento de Redução 1000A/800A - Comp. 624 x 624
A05-HB3323	4	ER 60-1730	Elemento Reto 1000A - Comp. 1730
A04-HB3323	3	ED1 60-3000-300	Elemento de Derivação 1000A - Comp. 3000 - Plugue 300
A03-HB3323	1	ER 60-2598	Elemento Reto 1000A - Comp. 2598 - Fechamento
A02-HB3323	3	ER 60-3000	Elemento Reto 1000A - Comp. 3000
A01-HB3323	1	FLP 60-100	Flange Padrão - 1000A - Comp. 100
Código	QTD	Referência	Descrição

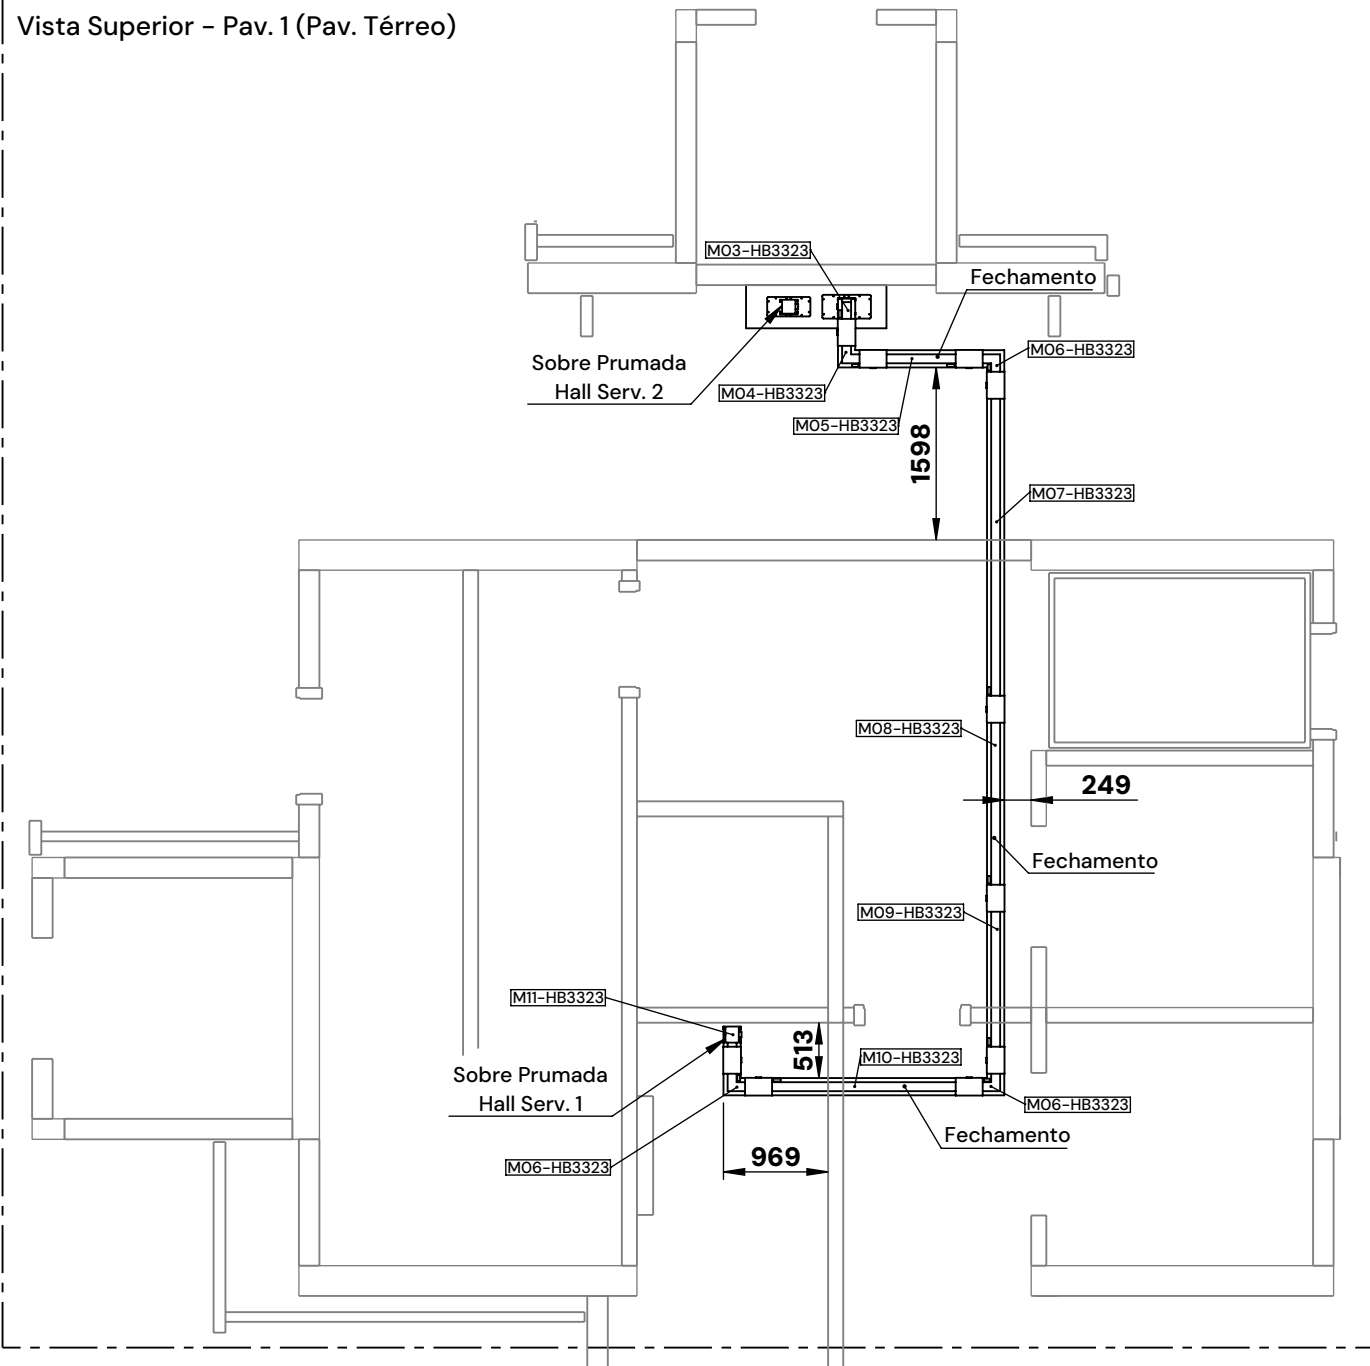

CLIENTE: PLANGENGE	DESENHISTA: Isabelly	FOLHA: 1/1
OBRA: ALMAH	PROJETO: HB 3323	
TÍTULO: Detalhamento Do Percurso do Barramento Blindado	DATA DO DESENHO: 15/05/2026	REVISÃO: A
	APROVADOR: Silvío - CREA 0685017163	ASSINATURA:
	DATA DA APROVAÇÃO:	